


SYMBOL LEGEND

- FEMA LIMITS (PER NFHL DATA)  
--- FLOWLINE  
--- WIRE FENCE  
○ FOUND SURVEY MONUMENT  
● SET SURVEY MONUMENT

| CURVE | RADIUS   | ARC LENGTH | CHORD LENGTH | CHORD BEARING | DELTA ANGLE |
|-------|----------|------------|--------------|---------------|-------------|
| C1    | 3064.79' | 1396.96'   | 1384.90'     | S 62°11'54" W | 26°06'57"   |

| LINE | BEARING       | DISTANCE |
|------|---------------|----------|
| L1   | S 77°38'07" W | 291.01'  |
| L2   | N 03°22'32" W | 50.62'   |
| L3   | S 02°43'24" E | 119.57'  |

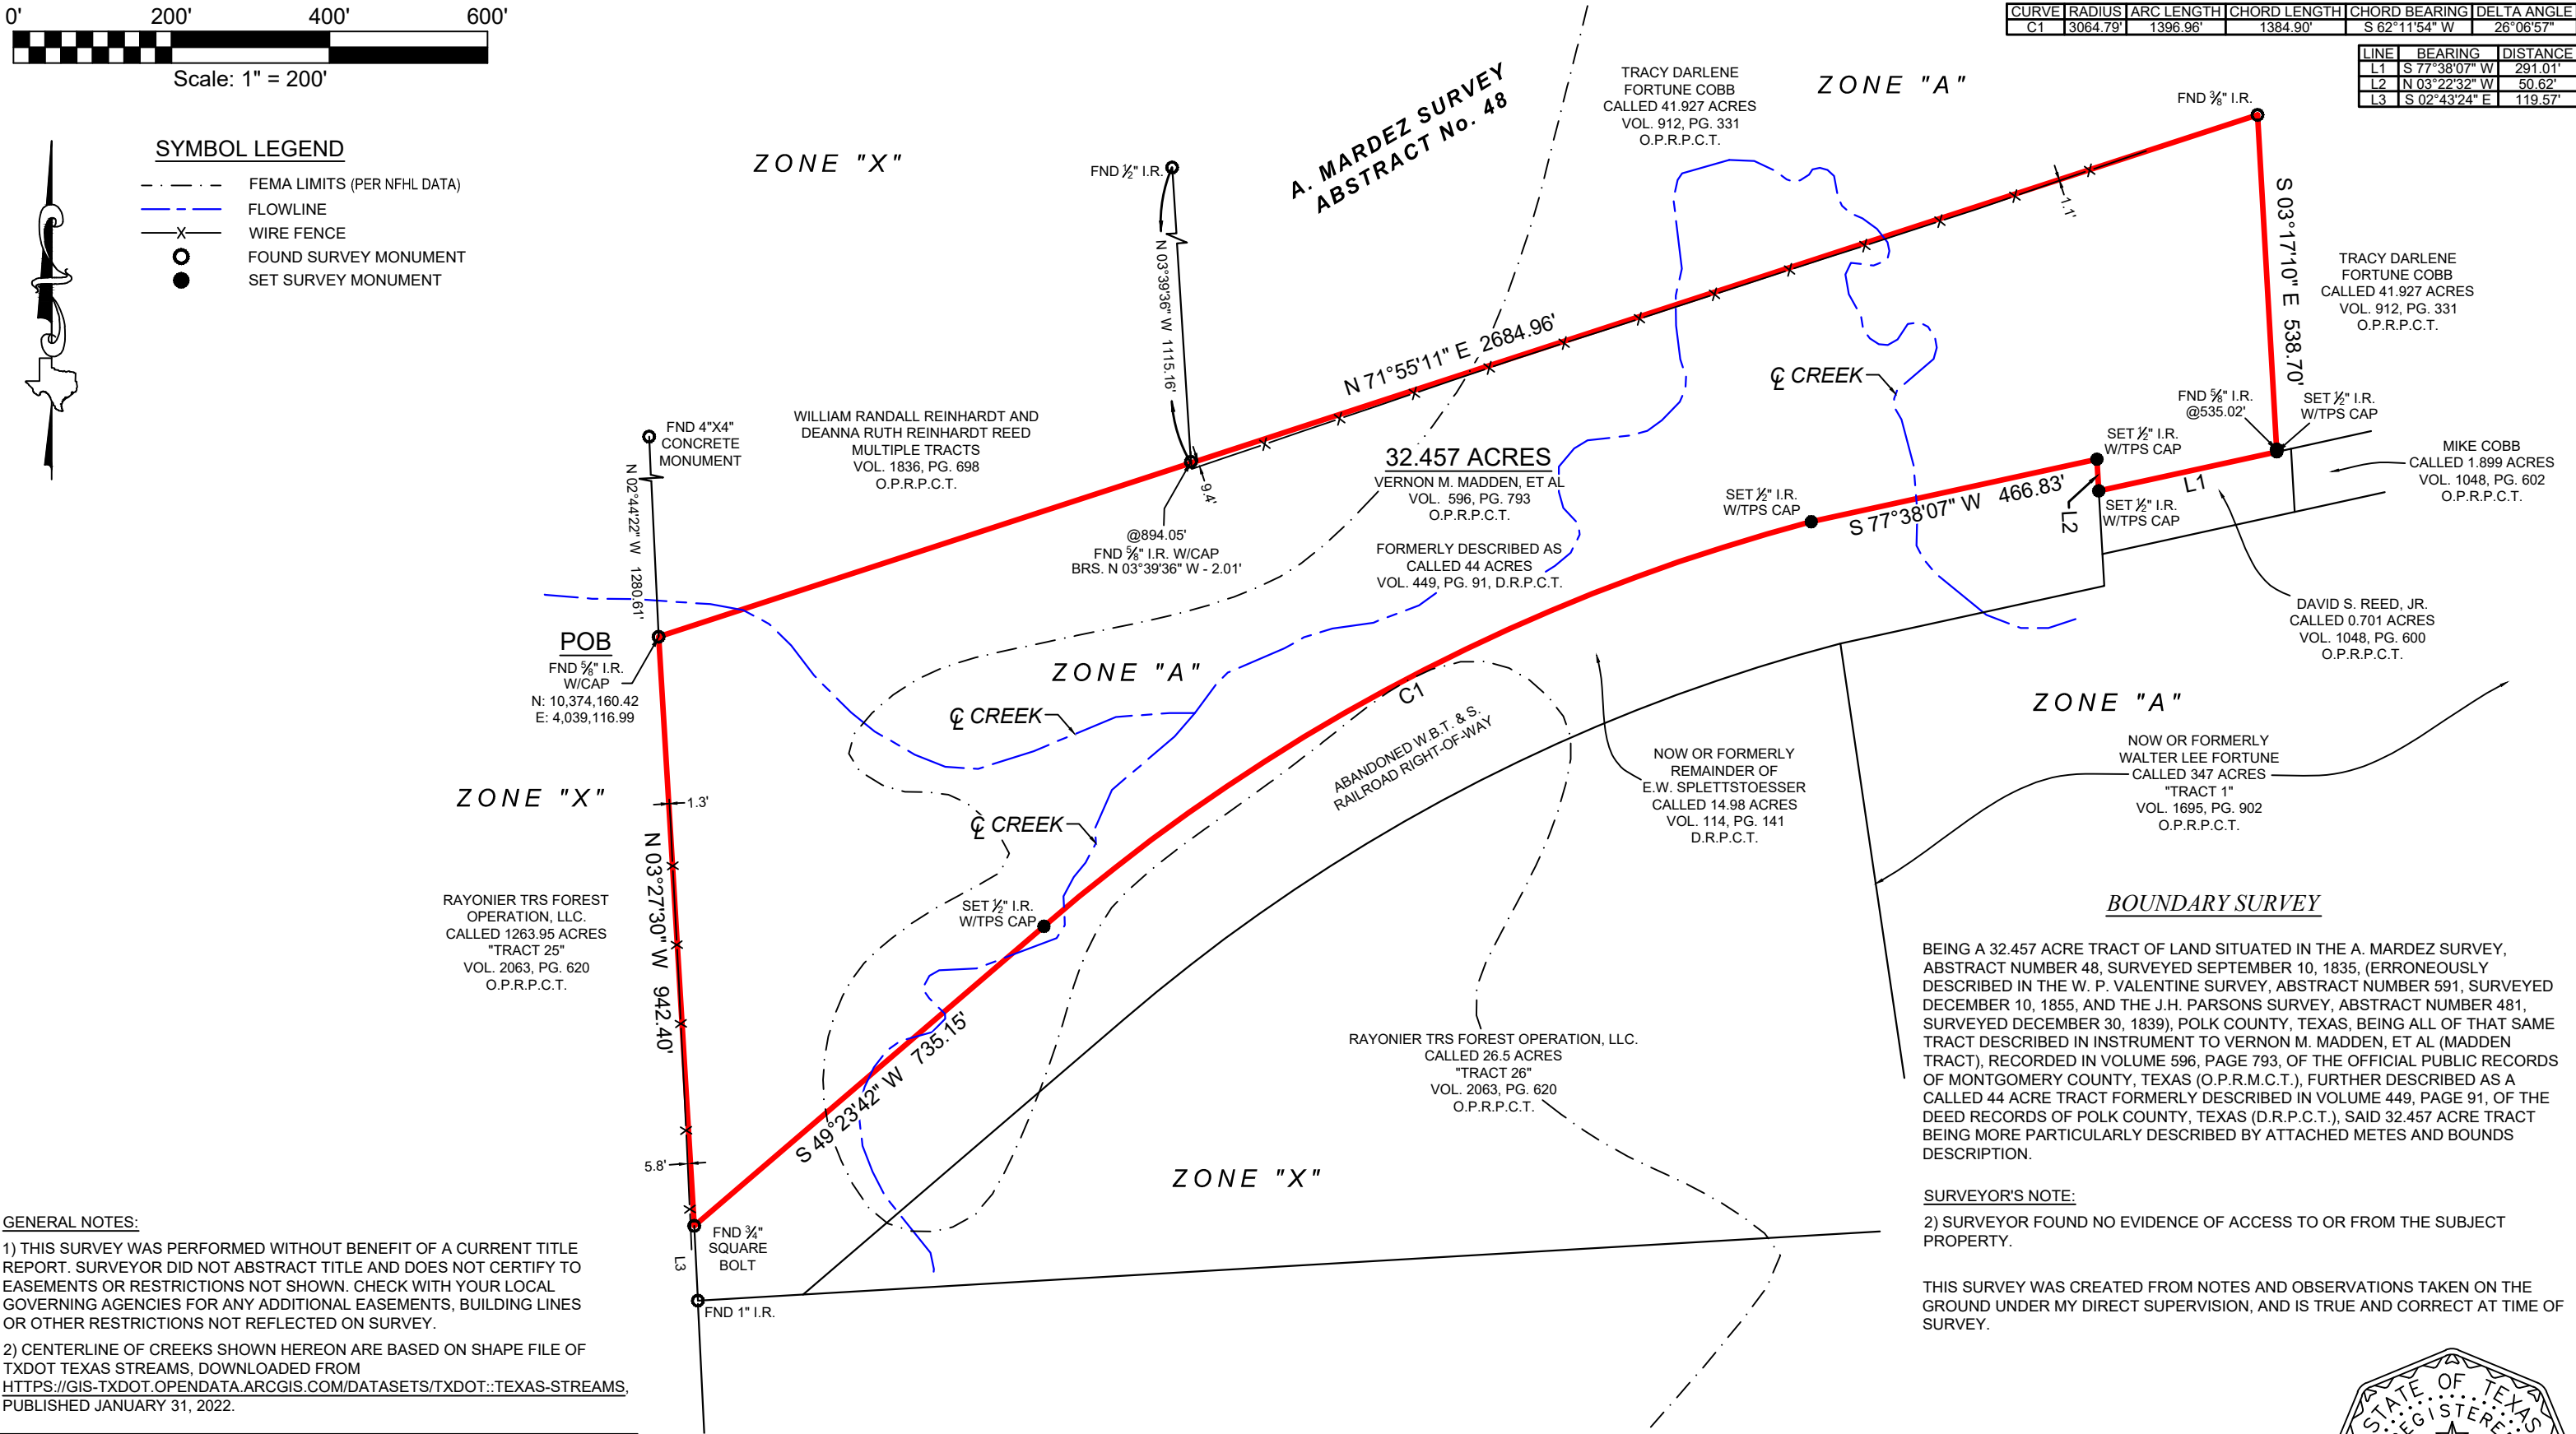

GENERAL NOTES:

- 1) THIS SURVEY WAS PERFORMED WITHOUT BENEFIT OF A CURRENT TITLE REPORT. SURVEYOR DID NOT ABSTRACT TITLE AND DOES NOT CERTIFY TO EASEMENTS OR RESTRICTIONS NOT SHOWN. CHECK WITH YOUR LOCAL GOVERNING AGENCIES FOR ANY ADDITIONAL EASEMENTS, BUILDING LINES OR OTHER RESTRICTIONS NOT REFLECTED ON SURVEY.
- 2) CENTERLINE OF CREEKS SHOWN HEREON ARE BASED ON SHAPE FILE OF TXDOT TEXAS STREAMS, DOWNLOADED FROM [HTTPS://GIS-TXDOT.OPENDATA.ARCGIS.COM/DATASETS/TXDOT::TEXAS-STREAMS](https://gis-txdot.opendata.arcgis.com/datasets/txdot::texas-streams), PUBLISHED JANUARY 31, 2022.

BOUNDARY SURVEY

BEING A 32.457 ACRE TRACT OF LAND SITUATED IN THE A. MARDEZ SURVEY, ABSTRACT NUMBER 48, SURVEYED SEPTEMBER 10, 1835, (ERRONEOUSLY DESCRIBED IN THE W. P. VALENTINE SURVEY, ABSTRACT NUMBER 591, SURVEYED DECEMBER 10, 1855, AND THE J.H. PARSONS SURVEY, ABSTRACT NUMBER 481, SURVEYED DECEMBER 30, 1839), POLK COUNTY, TEXAS, BEING ALL OF THAT SAME TRACT DESCRIBED IN INSTRUMENT TO VERNON M. MADDEN, ET AL (MADDEN TRACT), RECORDED IN VOLUME 596, PAGE 793, OF THE OFFICIAL PUBLIC RECORDS OF MONTGOMERY COUNTY, TEXAS (O.P.R.M.C.T.), FURTHER DESCRIBED AS A CALLED 44 ACRE TRACT FORMERLY DESCRIBED IN VOLUME 449, PAGE 91, OF THE DEED RECORDS OF POLK COUNTY, TEXAS (D.R.P.C.T.), SAID 32.457 ACRE TRACT BEING MORE PARTICULARLY DESCRIBED BY ATTACHED METES AND BOUNDS DESCRIPTION.

SURVEYOR'S NOTE:

- 2) SURVEYOR FOUND NO EVIDENCE OF ACCESS TO OR FROM THE SUBJECT PROPERTY.

THIS SURVEY WAS CREATED FROM NOTES AND OBSERVATIONS TAKEN ON THE GROUND UNDER MY DIRECT SUPERVISION, AND IS TRUE AND CORRECT AT TIME OF SURVEY.

**TEXAS PROFESSIONAL SURVEYING**  
3032 N. Frazier, Conroe, Texas 77303  
Ph: 936.756.7447 Fax: 936.756.7448  
[www.surveyingtexas.com](http://www.surveyingtexas.com)  
Firm No. 10083400

|            |                |
|------------|----------------|
| PROJECT    | 37585_32.457AC |
| FIELD DATE | 07/15/2024     |
| DRAWN BY   | EV             |
| CHECKED BY | ET / CPP       |
| FIELD CREW | JN             |
| REV 1      | ---            |
| REV 2      | ---            |
| REV 3      | ---            |
| REV 4      | ---            |

PURCHASER .....  
ADDRESS .....CORRIGAN, TX, 75939  
SURVEY .....A. MARDEZ, A - 48  
SUBJECT .....32.457 ACRES  
COUNTY .....POLK

A PORTION OF THIS PROPERTY APPEARS TO LIE WITHIN THE 100 YEAR FLOODPLAIN, PER GRAPHIC SCALING OF FEMA FIRM PANEL NO. 48373C0075C, HAVING AN EFFECTIVE DATE OF 09/03/2010

ALL COORDINATES, BEARINGS, DISTANCES, AND AREAS SHOWN HEREON ARE GRID MEASUREMENTS BASED ON GPS OBSERVATIONS AND REFERENCED TO THE NORTH AMERICAN DATUM OF 1983 (NAD83), TEXAS STATE PLANE COORDINATE SYSTEM, CENTRAL ZONE, U.S. SURVEY FEET.

Thomas A. McIntyre  
Registered Professional Land Surveyor No. 6921

